




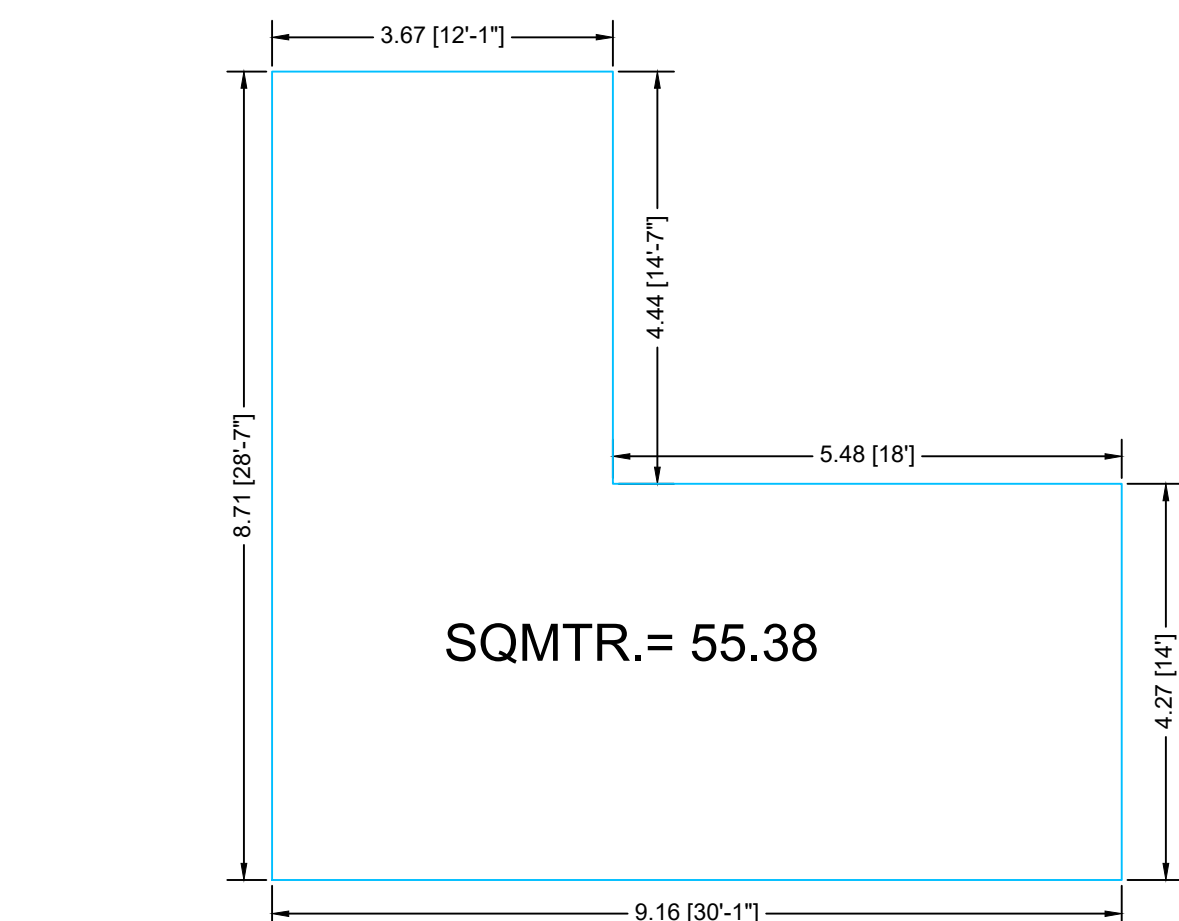


PARKING PLAN

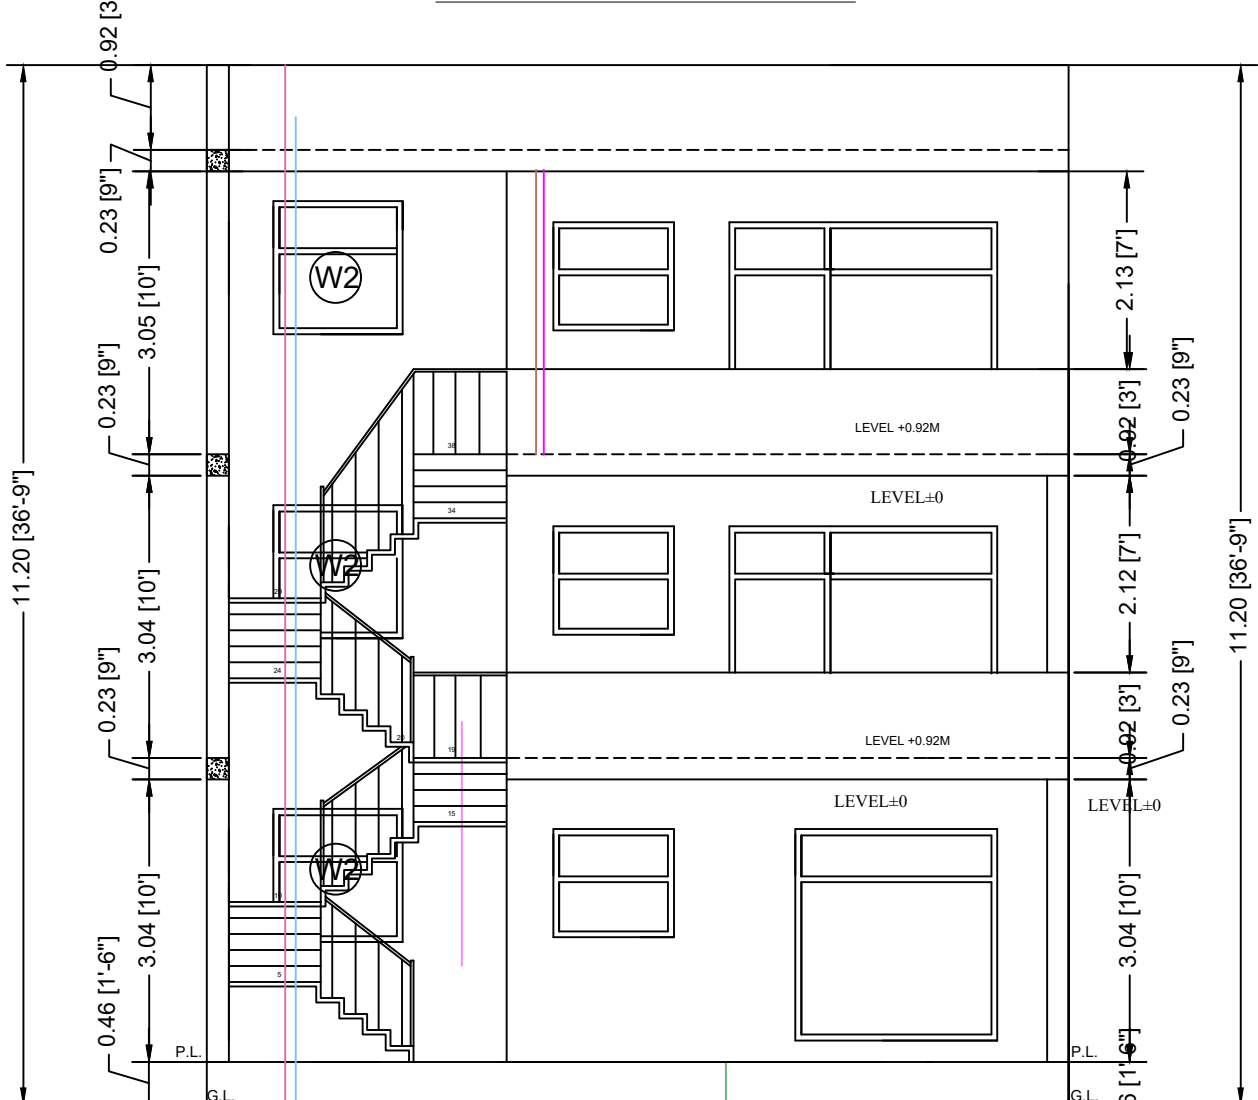


FRONT ELEVATION

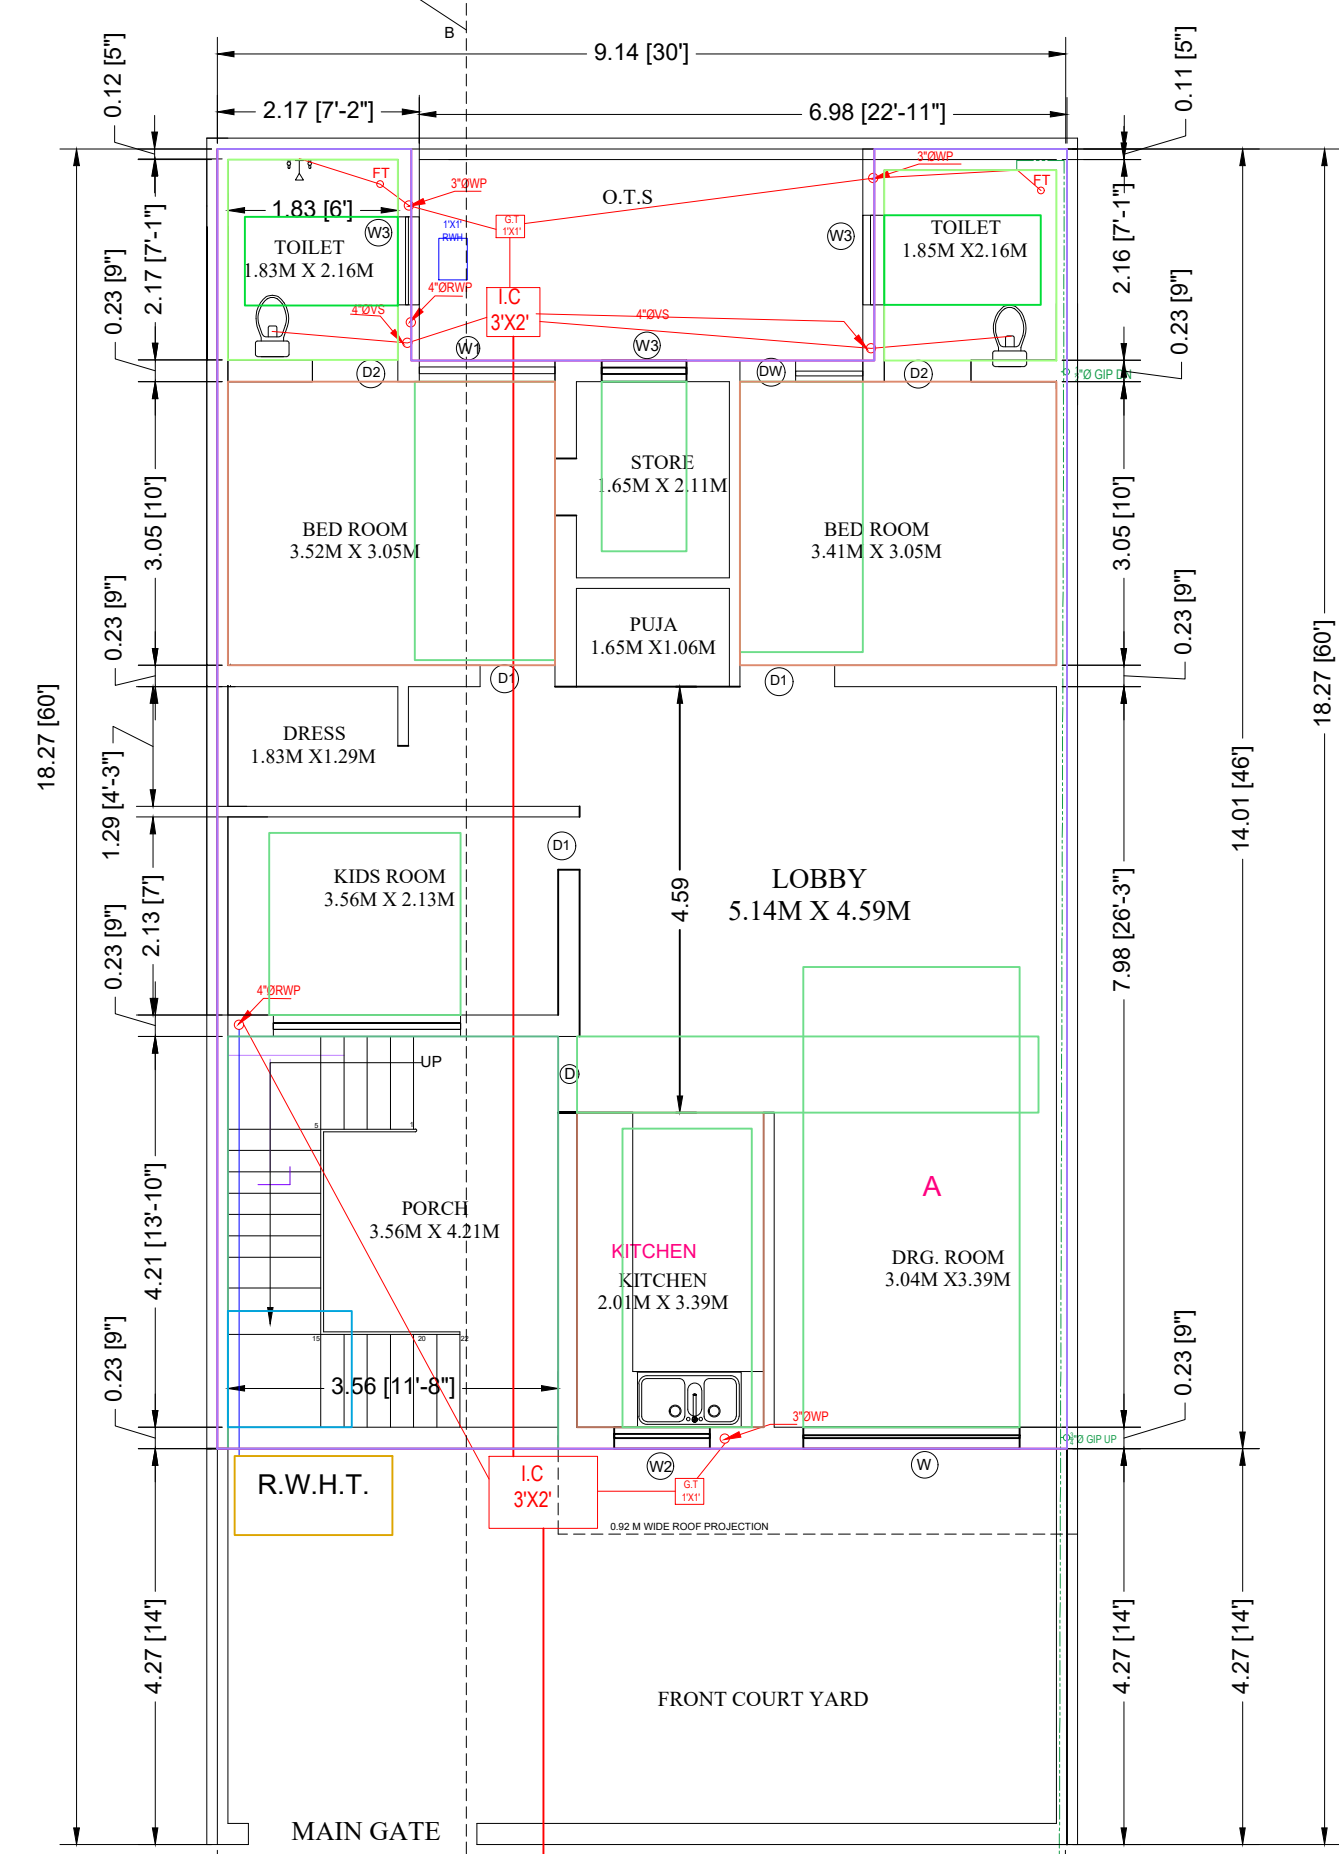


GROUND FLOOR PLAN

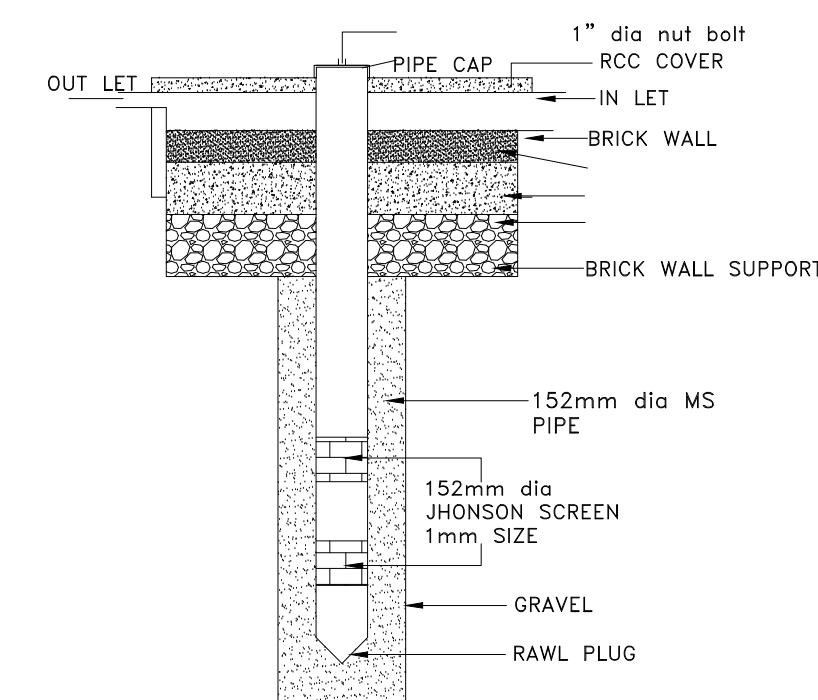


SECTION
RAIN WATER HARVESTING PIT

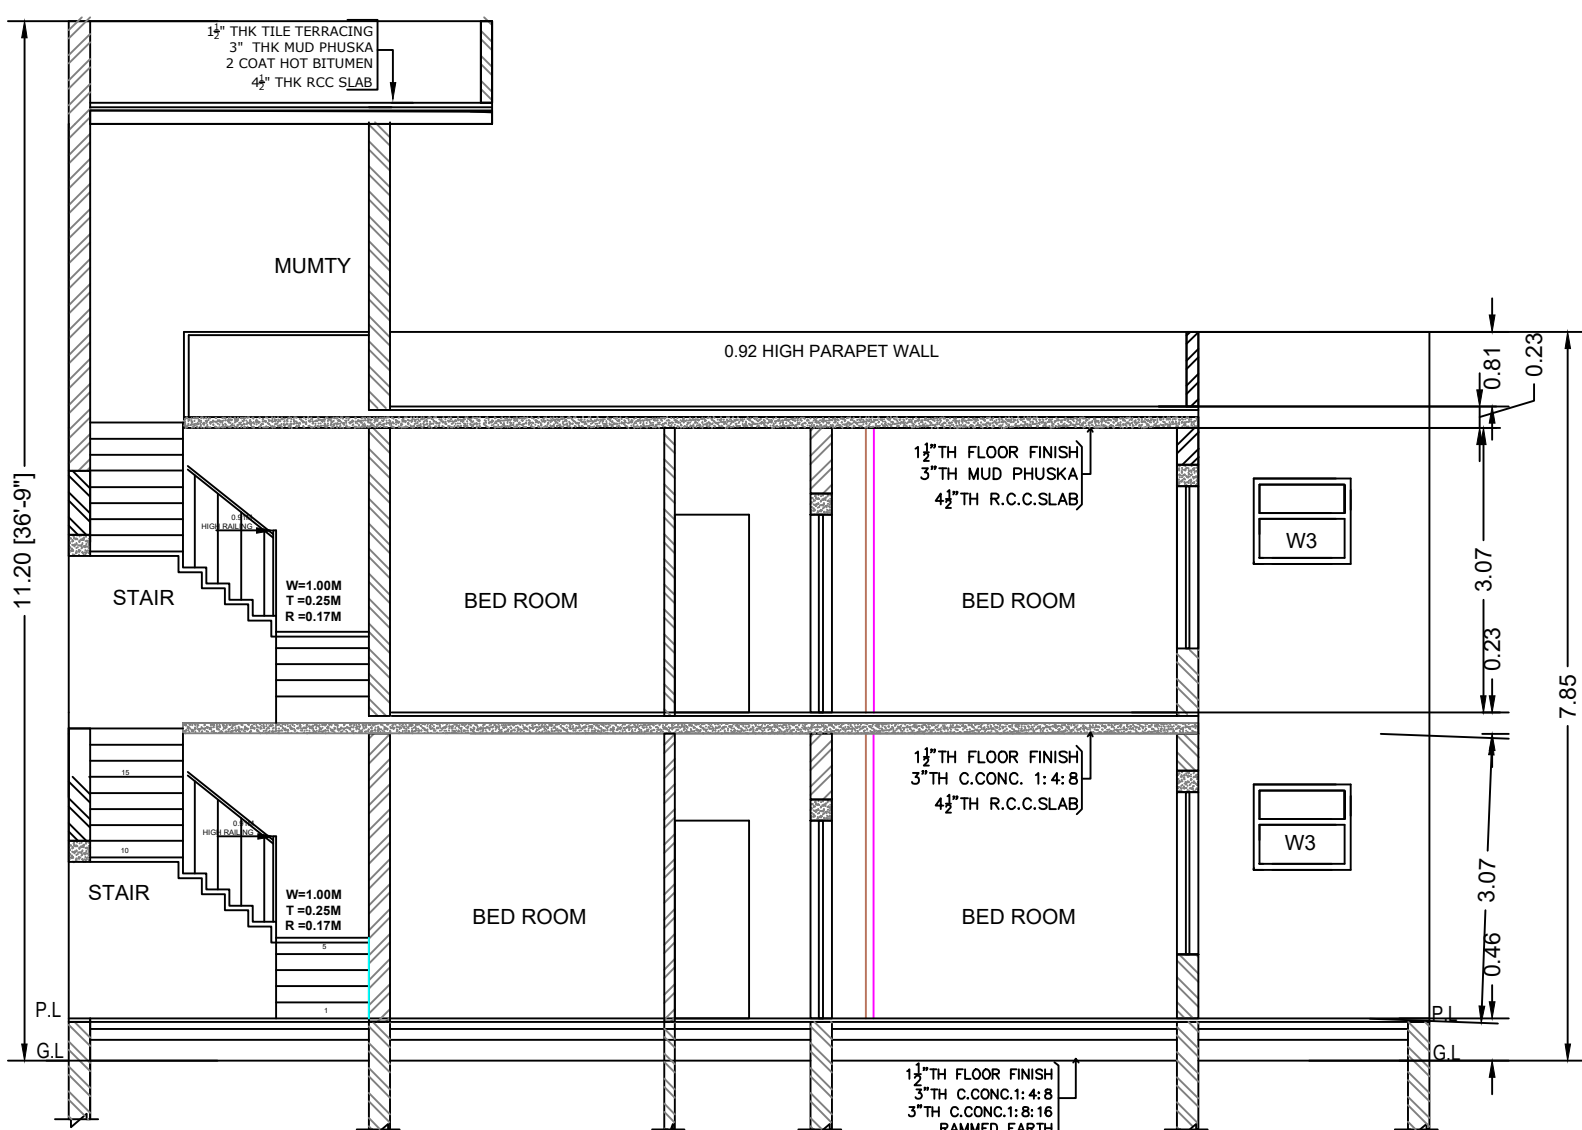

SECTION A-B

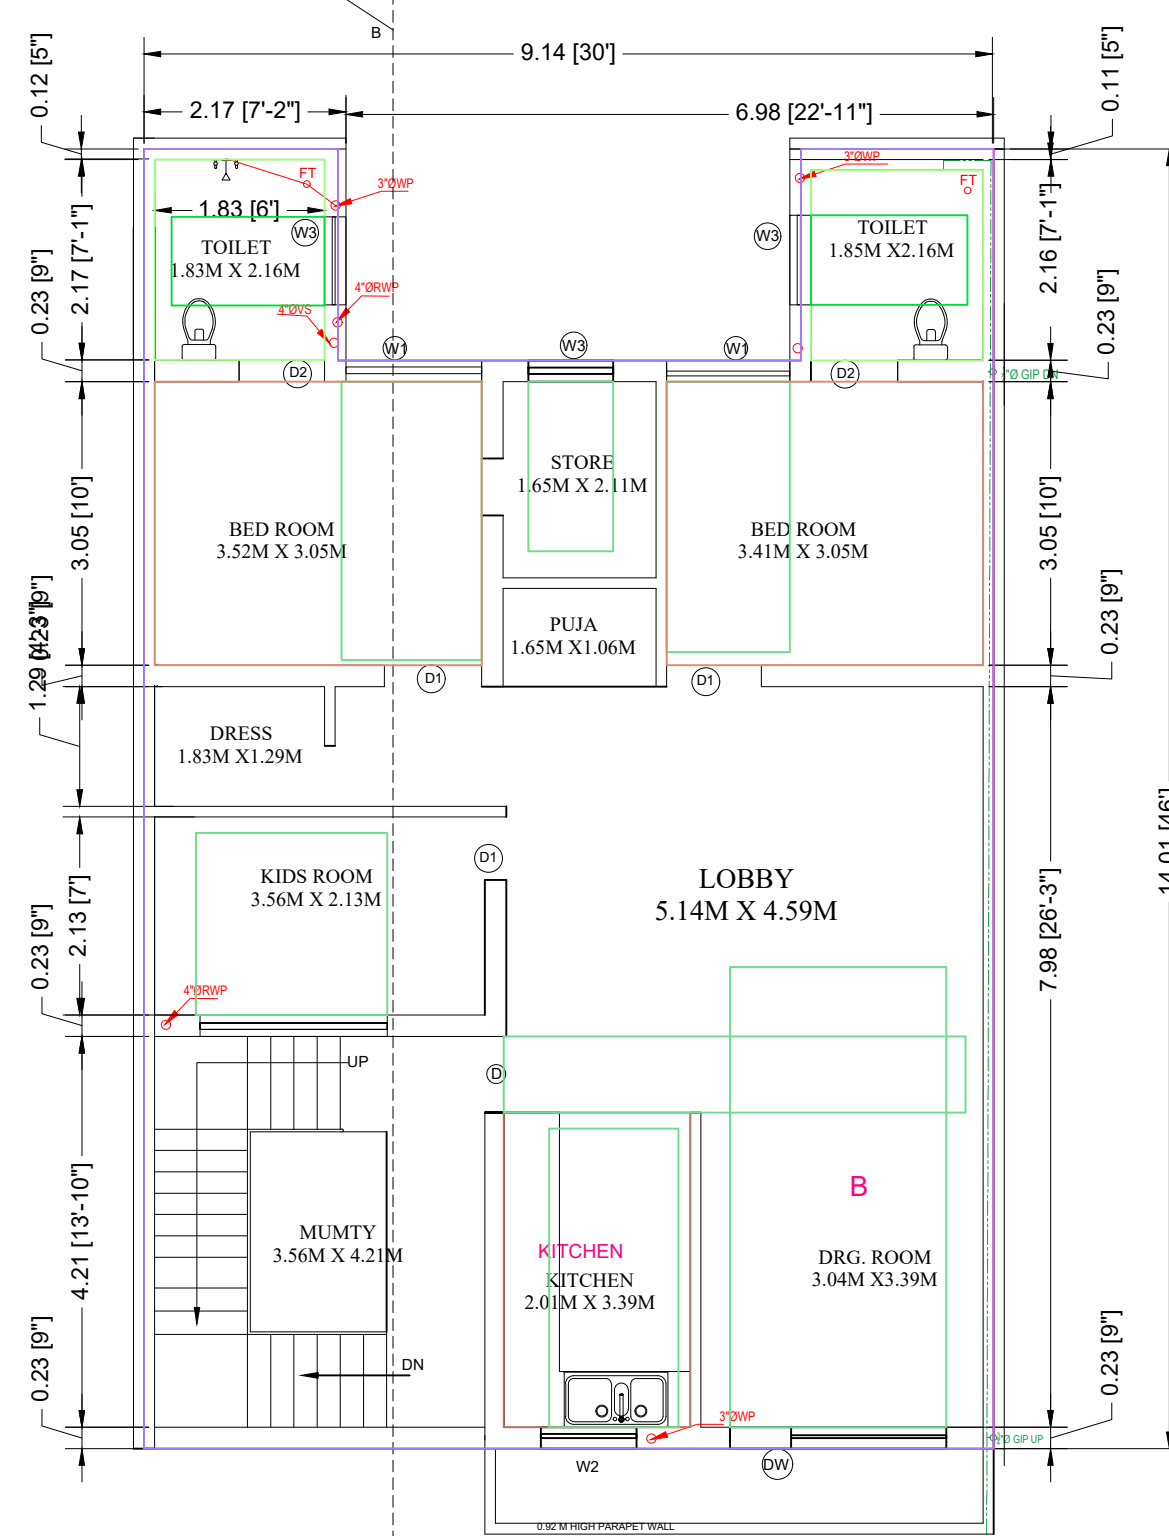

FIRST FLOOR PLAN

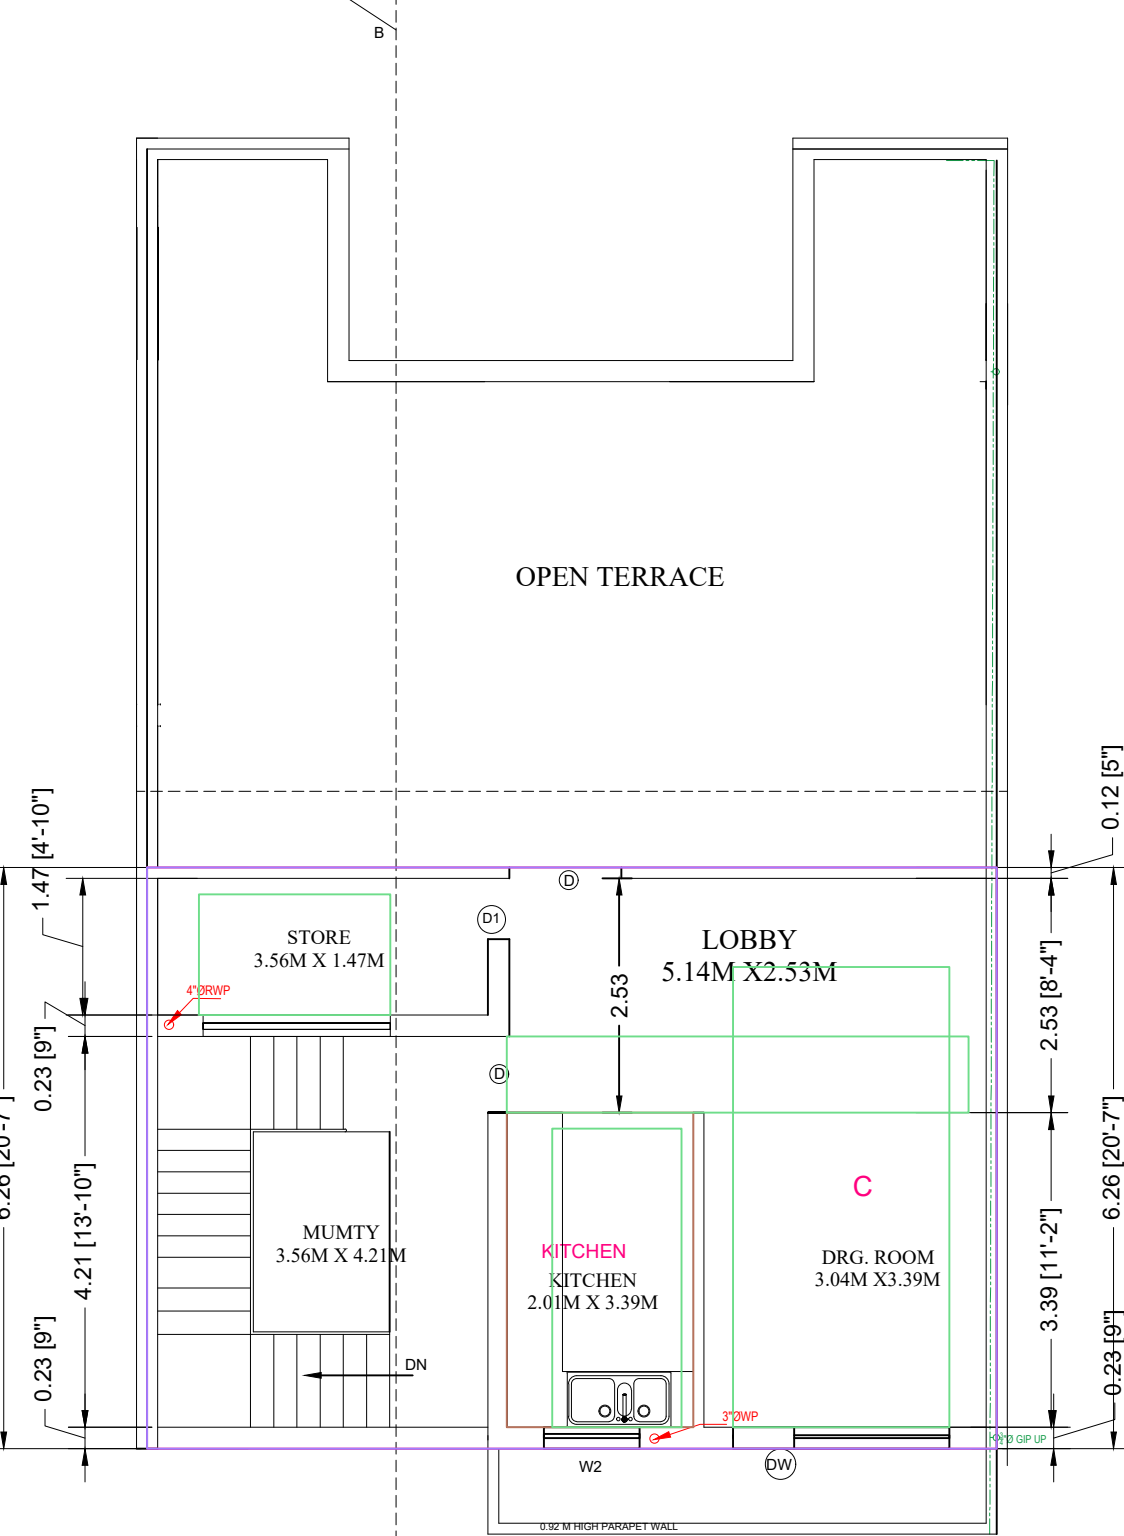


SECOND FLOOR PLAN




SUPER IMPOSE

HOUSE OF OTHER OWNER

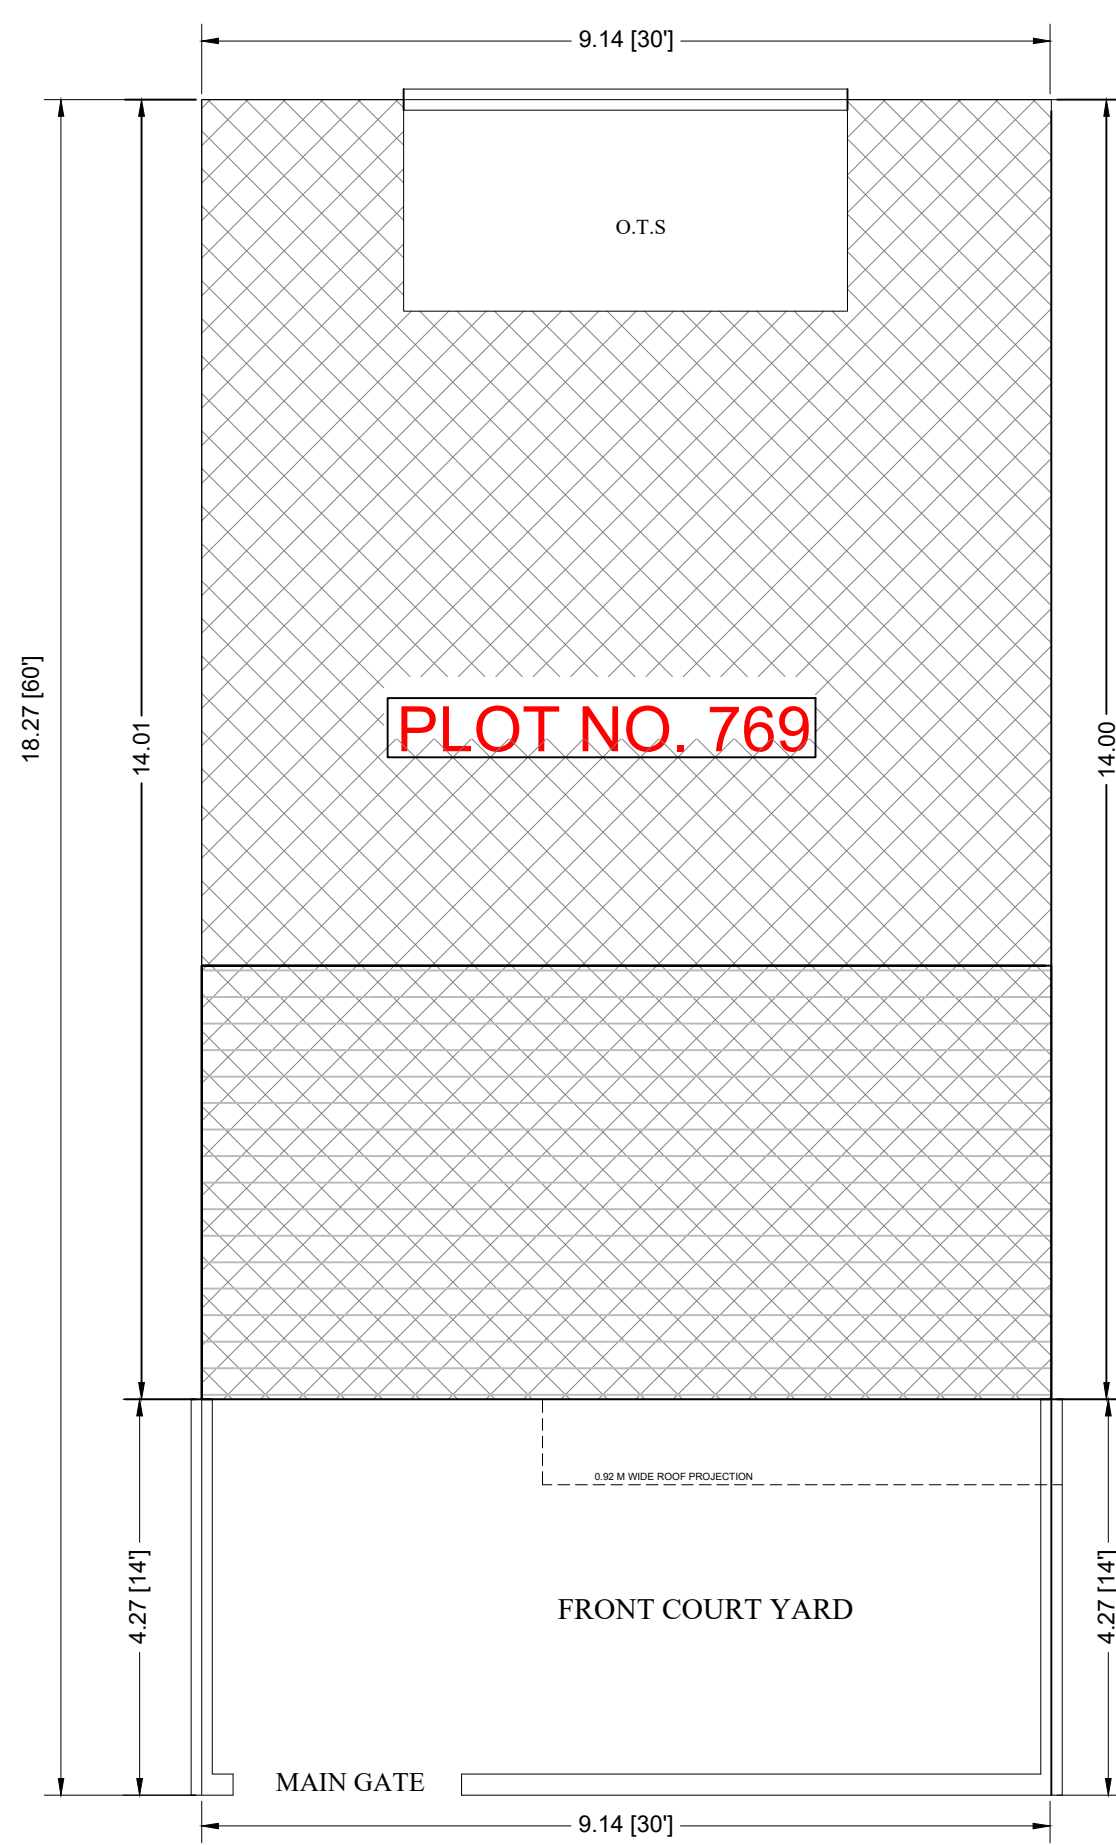


SITE PLAN

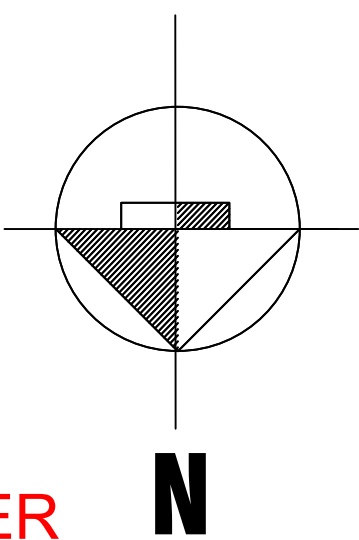

OTHER OWNER

OTHER OWNER

SITE

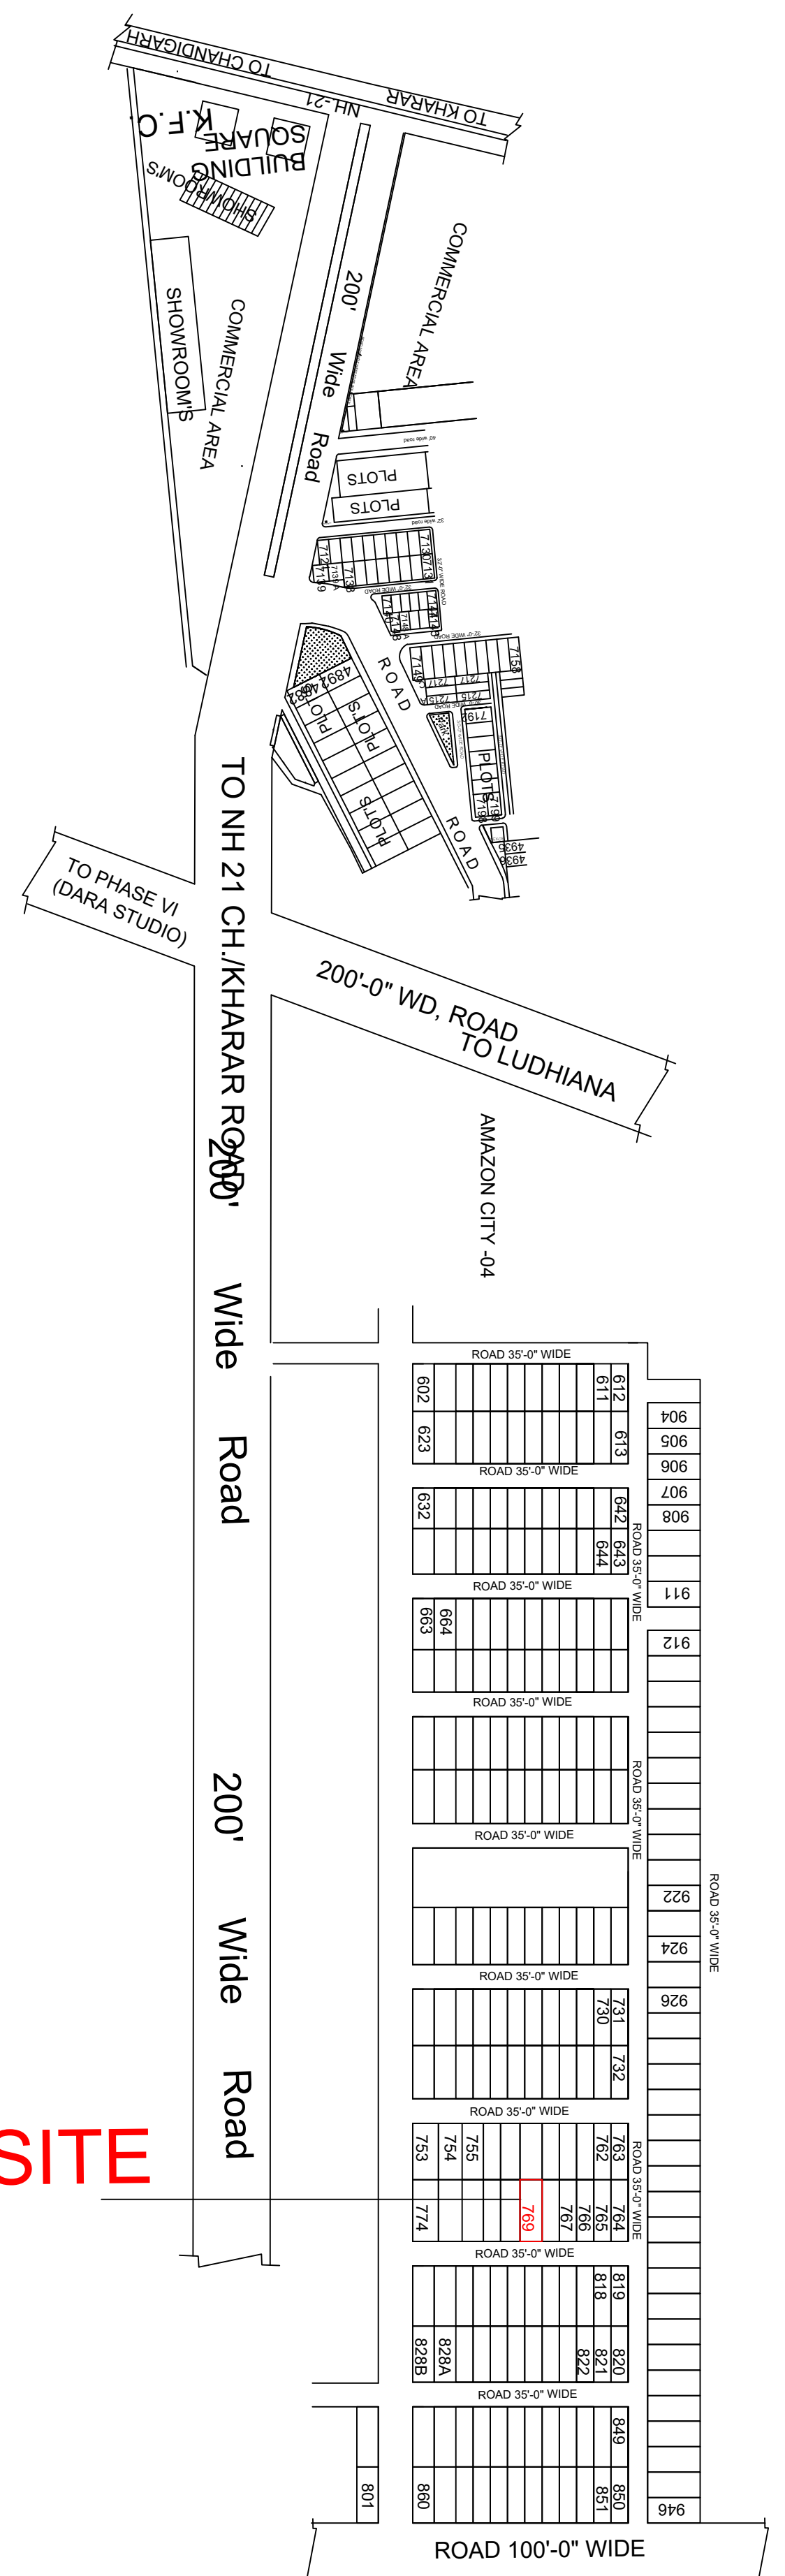

LOCATION PLAN

PROPOSED PLAN FOR THE HOUSE OF
SMT. SHALINI AGGARWAL
W/O SH. MUNISH AGGARWAL
AT PLOT NO 769,AMAZON CITY
SECTOR-123,RAKBA- JANDPUR
TEHSIL- KHARAR,DISTT. S.A.S. NAGAR.

APPLICATION NO:- PB/SAS/KHARA/250949

AREA STATEMENT

TOTAL PLOT AREA= 30'-0"X60'-0",
= 1800 SQFT = 200 SQYDS
= 167.22 SQ MTR.

F.A.R PERMISSIBLE:-1:1.75

PROP. GROUND FLOOR COVED. AREA
= 116.85 SQ MTR (1257 SQ.FT.)

PROP. FIRST FLOOR COVED. AREA
= 116.85 SQ.MTR. (1257 SQ.FT.)

PROP. SECOND FLOOR COVED. AREA
= 57.32 SQ.MTR. (616.98 SQ. FT.)

TOTAL PROPOSED F.A.R. AREA
=116.85+116.85+57.32 = 291.02 SQ.M.OR 3130.98 SQ.FT.

PARKING AREA= 55.38 SQ.MTR. (596.10 SQ.FT.)

BOUNDARY WALL= 48'-0" R. FT.(14.62 R.MTR.)

PARAPET WALL = 76'-0" R.FT.(23.16 R.MTR.)

TOTAL COVD AREA:-
= 3130.98 SQFT =291.02 SQ. MTR.

F.A.R ACHIEVED :-1:1.739

TABLE:

S.NO.	PARTICULAR	AS PER BYE-LAWS	AS PER SITE
1.	G.F. COVD. AREA	70%	69.83%
2.	F.F. COVD. AREA	70%	69.83%
3.	S.F. COVD. AREA	—	34.27%
4.	FRONT SET BACK	2.16 M	4.04 M
5.	REAR SET BACK	—	—
6.	HEIGHT	50'-0"	11.20 M


JOINERY SCHEDULE

S.NO.	NAME	SIZE	SILL LVL.	LINTEL LVL.
1	DW	0.76M+0.63M X 2.51M+1.82M	0", 0.68M	2.51M
2	DW1	0.92M+1.80M X 2.51M+2.28M	0", 0.23M	2.51M
3	D	1.07M X 2.51M	0"	2.51M
4	D1	0.92M X 2.13M	0"	2.13M
5	D2	0.76M X 2.13M	0"	2.13M
6	W	2.18M X 2.28M	0.23M	2.51M
7	W1	0.67M X 1.82M	0.68M	2.51M
8	W2	1.39M X 1.29M	1.21M	2.51M
9	W3	0.83M X 0.92M	1.60M	2.51M
10	W4	1.28M X 1.82M	0.68M	2.51M

NOTES:-

1. ALL PIPES SHOULD BE USED AFTER SMOKE TEST.
2. ALL 4" THICK WALLS SHALL HAVE 9"X9" RCC BEAMS OVER THEM.
- 3.MAIN GATE AND BOUNDARY WALL SHALL BE CONSTRUCTED AS PER THE STANDARD DESIGN.
- 4.ALL SANITARY WORK SHALL BE GOT DONE FROM A GOVERNMENT APPROVED PLUMBER.
- 5.NO TOILET/WC SHALL BE LOWER THAN THE PLINTH LEVEL OF THE BUILDING.
- 6.STRUCTURE STABILITY OF THE BUILDING IS RESPONSIBILITY OF THE OWNERS.

OWNER	ARCHITECT
NAME OF ARCHITECT	RAM LAL
FIRM NAME	ARCHITECT DESIGN STUDIO
MOBILE NO.	85568-64729
REGISTRATION NO.	266

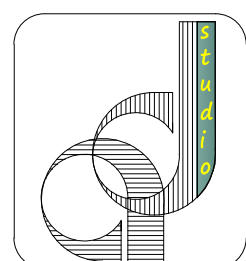

Architect Design Studio
ARCHITECTS, VALUERS & INT.DESIGNERS
Shop No. 6, G. Floor, Ambika Complex
Opp. Khadi Bhandar, Kharar
Mobile : 8556864729,8284810107.
email : architectdesignstudio777@gmail.com